

REQUEST FOR PROPOSAL AGAINST TENDER ENQUIRY IN TWO BID SYSTEM

2447/26-27/OPW dt 09 Jun 2026

REQUEST FOR PROPOSAL (RFP) OF SUPPLY OF THREE (03) x LARGE STORE SHELTER JOB NO:- OT/EC/4/5/26-27/2447

1. The Online bids under Open Tender Enquiry (Two Bid System) are invited from the GeM registered vendor by 121 Engineer Regt for and on behalf of the President of India for Supply of Items in **Part-II**. The tender reference under is 2447/RFP/26-27/OPW dt **09 Jun 2026** and can be viewed in GeM portal. The bidders will ensure factors of **Quantity, Quality and Timeline** in execution of the project and adhere to instruction mention in RFP in correct letter in spirit.

2. The address of seeking clarification regarding this RFP are given below:-

- 2.1 Quotation/Quires to be address to - Commanding Officer
121 Engineer Regiment
Pin – 914121
c/o 99 APO
- 2.2 Postal address for sending the Quotation- 121 Engineer Regiment
Pin – 914121
c/o 99 APO
- 2.3 Name/Designation of Contact Personnel - EPO,121 Engineer Regiment

3. Instructions/Conditions. Your online offer for Supply of **Three (03) x Large Store Shelter** at following locations shall be submitted as follows:-

3.1 **Three (03) x Large Store Shelter:** Distr of the job is as tabulated below:

S.No	Job No	Asset	Qty	Delivery Loc
3.1.1	2447	Large Store Shelter	03	Nakyo GG, Arunachal Pradesh

3.2 Bids should be uploaded/ submitted through GeM Portal. The uploaded bids will be opened as per the schedule of GeM activities.

3.3 Type of Job. **Supply of Stores.**

4. The RFP is divided into 3 Parts as under:-

- 4.1 Part I. Additional Terms & Conditions.
- 4.2 Part II. Technical Specifications and drawings with complete store list.
- 4.3 Part III. Organisation specific Terms & Conditions.

5. Bidders are requested to read the RFP carefully and adhere to the instructions.

6. The RFP is being issued with no financial commitment and the Buyer reserves the right to change or vary any part thereof at any stage. Buyer reserves the right to withdraw the RFP, should it become necessary at any stage.

PART-1 : ADDITIONAL TERMS AND ONDITIONS

1. The **Supply of Three (03) x Large Store Shelter** is required in **Gen Area of Nakyo GG, Arunachal Pradesh**. The tenderers/ bidders are advised to take prior appointment with the **Commanding Officer, 121 Engineer Regiment** prior to site visit. The bids submitted by the Vendor / Firm should be based on **prior site survey and assessment of connectivity & transportation conditions**.

2. **Submission of Documents for Technical bid.** Interested bidders shall submit the bids along with all requisite documents on GeM Portal as per fixed timelines. If any bidder fails to submit, any of the documents as mentioned in this paragraph, under suitable heads on GeM, his/her bid will be treated as **rejected**. Scanned copy of the following documents will be uploaded online on GeM Portal for **Technical Bid**:-

2.1. **Non-disclosure Certificate.** Certificate for Non-disclosure of Contract Documents. All documents / drawing / specification shall remain confidential and to be disseminated restrictively for the sole purpose of executing order. In this regard, a certificate shall be submitted as per **Appendix 'A'** attached.

2.2. **Tender Conditions Acceptance Certificate.** The bidder shall certify for acceptance of all the tender conditions of the online RFP and furnish a certificate as per **Appendix 'B'**. The certificate duly signed shall be scanned and uploaded. In case of deviations, the bid shall be rejected. If legally authorized signatory signs the certificate, a copy of the legal authorization letter will be enclosed & uploaded online as well.

2.3. **Bid Security Declaration.** The bidder shall furnish a certificate as per **Appendix 'C'** regarding the non-withdrawal or modification of the bid during the period of validity. If legally authorized signatory signs the certificate, a copy of the authorization letter will be enclosed & uploaded online as well. The certificate duly signed shall be scanned and uploaded. In case of deviations, the bid shall be rejected. If any bidder withdraws or modifies his/her bid during the period of validity, the bidder will be suspended for a period of one year.

2.4. **Affidavit for Submission of Original/Genuine/untampered Documents.** Any editing / tampering to any Certificates / documents, Terms and Conditions, Technical Specification or any part of the tender or submission of any forged /fake documents while technical bid, will lead to rejection of bid. Such bidder/ vendor will become liable for penal actions as per directions of higher HQ and the bidder will be suspended for a period of one year. **In this regard, the bidder must submit an affidavit in prescribed format as per Appendix 'D' on non-judicial stamp paper duly notarized.** Bidder failing to submit the affidavit will be treated as **rejected**.

2.5. **Contract Assurance Certificate.** The bidder will submit a certificate assuring the Supply of **Three (03) x Large Store Shelter** as per technical specification within stipulated period as per **Appendix 'E'**.

2.6. **Affidavit for Not being Blacklisted / Banned.** The bidder must submit an affidavit in prescribed format as per **Appendix 'F'** on non-judicial stamp paper duly notarized stating that the firm has not been **blacklisted / banned** and **No LD Charges** has been imposed on his / her firm in past 5 financial years from any Central /State Govt Department.

2.7 **Site Visit Certificate.** Due to the remote location and operational nature of work, bidders are advised to visit the site before submission of bid to understand site conditions, accessibility, logistics and execution constraints. The bidder shall submit along with the technical bid a site visit report duly signed by the bidder and acknowledged by the user unit representative, tentative methodology of execution, deployment plan of plant and machinery, **tentative layout / conceptual drawings** in metric units and **tentative materials / store list** based on the technical specifications, calculations and **tentative design / details provided in the bid documents**. The submitted documents / drawings should indicate essential details relevant to the scope of work for assessment of technical understanding and feasibility of execution. Non-submission of the above documents shall render the bid liable for rejection during technical evaluation. Non-familiarity with site conditions after placement of supply order / contract shall not be accepted as grounds for extra claims or extension of time. In this regard, a

certificate as per **Appendix 'G'** attached shall be submitted.

2.8 Vendor should accommodate the suggested changes as per functional requirement of user during the course of project. The vendor need to furnish undertaking certificate to this effect as per **Appendix 'H'** confirming to this clause during bidding.

2.9. **EMD.** The supplier will deposit **3% EMD** of tender amount along with the tender documents in form of DD/FDR/TDR(Upload a copy) issued from any nationalized bank in favour of Commanding Officer, 121 Engineer Regiment or exemption proof, if exempted (NSIC Registration Certificate required for MSME, it should be registered with NSIC under its single point registration scheme).

2.10. Bidder must upload ATC including any corrigendum (if issued) **duly stamped and signed** on each page by the proprietor / legally authorized signatory of the firm concerned.

2.11. **No Outstanding Tax Liability Certificate.** The bidder will submit a no outstanding tax liability certificate duly authenticated by authorized CA for past three (03) financial years. Bidders not complying this condition will be rejected during the tech bid.

2.12 **Annual Turnover Certificate.** The minimum average annual turnover of the bidder during the last three years, ending on 31 March of the previous financial year, should be more than 50% on total tender value. Documentary evidence in the form of certified audited balance sheets of relevant periods or a certificate from the Chartered Accountant/Cost Accountant indicating the turnover details for the relevant period shall be uploaded with the bid. In case the date of constitution incorporation of the bidder is less than 3 year-old, the average turnover in respect of the completed financial years after the date of constitution shall be taken into criteria.

2.13. **Income Tax Return.** The bidder shall upload last three (03) years income tax return duly verified by authorized CA.

2.14. **Balance Sheet.** The bidder shall upload audited balance sheet of Last three (03) years duly verified by authorized CA.

2.15. **Proof of Experience.** Firms with experience of supply of same or similar nature of work in past three financial years in the NE region (especially Assam & Arunachal Pradesh) will be given preference. Bidders must upload ink signed copy of relevant Supply order / Contract agreement, CRAC certificate, Completion Certificate and performance certificate as specified in subsequent subparagraphs as proof of experience. Firms not submitting the above-mentioned documents would be treated as disqualified and their bid would be rejected.

2.15.1. **Documents for Experience.** The bidder should have executed same or similar category/nature of work and submit copies of Supply/Work order issued by buyer organization of works in last three financial years along with the technical bid. Details of relevant contracts to be submitted are as follows: -

2.15.1.1. Single Supply order of at least **35%** of estimated bid value **or** two orders of at least **20%** each of estimated bid value .

2.15.1.2. The bidder must also furnish the relevant completion certificate /CRAC and photographs of the completed assets as the proof of experience.

2.16. **Past Performance.** Bidder should upload the Past performance certificate issued by respective buyer organization with SATISFACTORY or above remarks for the same/ similar work on supply of stores not less than 50% of the tender value. The works should carried out only within Arunachal Pradesh and Assam in AOR of HQ Eastern Comd region.

2.17. **Work Load Declaration .**The bidder must furnish the list of ongoing work in hand with cost of each work as on date of submission of bid in firm letterhead along with copy of work order/ supply order. Bidder failing to furnish the work load declaration will technically disqualified

2.18. Incidents raised against the sellers on GeM since last 24 months from the date of bid publish should be enclosed, else firms will be **rejected** during Technical Bid.

2.19. **Price Justification.** A price justification will be asked from bidder on GeM as and when L1 amount found below 20% of approved Technical Sanction amount. The bidder may be rejected

during Financial Evaluation if submitted justification is not found to be admissible or an additional amount of 10% of L1 value will be asked from vendor to deposit as Bank Guarantee.

2.20 **GSTIN Registration.** The bidder must upload a duly self-attested scanned copy of valid GST Registration of Firm/ Company.

2.21. The bidder must submit a valid latest **Solvency Certificate** issued by a National Bank (within last 6 Months) covering 50% of the tender value.

2.22. **Working capital** value from concerned bank of the bidder.

2.23. **Affidavit** regarding firm or involved in any **litigation/ arbitration** to be upload by the participant bidder.

2.24. Photocopy of **PAN Card** of the firm and owner duly self-attested.

2.25. **ISO** Quality Management System certificate (ISO 9001:2015)

2.26. **ISO** Environmental Management System Certificate (ISO 14001: 2015).

2.27. **ISO** Occupational health and safety management system certificate (ISO: 45001: 2018).

2.28. **OEM /OEM Authorization** The bidder should preferably be an OEM or OEM authorised dealer. Bidder must upload a valid OEM certificate along with the Tech Bid documents. In case of Non OEM bidder, the bidder must furnish a copy a legal MOU with the OEM as proof of OEM Authorization.

2.29. Banker's details alongwith **NEFT Form** duly authenticated by bank manager alongwith a copy of **cancelled cheque** to be uploaded.

2.30. **MII certificate** as per criteria fixed by the buyer.

2.31. **Termination/ Cancellation of Supply Order.** In the event of slow progress/ work not started against the Supply Order offered to you for those items shall be terminated/cancelled instantly with respect to following work progress:-

2.31.1. Supply not started within 01 month (30 days) after issuing work order.

2.31.2. Overall 50% of stores not delivered within 45 days after issuing work order.

NOTE:- In the event of breach of contract on any account or no supply of materials or delay in supply of stores, Commanding Officer, 121 Engineer Regiment shall have the **right to cancel the supply order** and purchase the stores at your **RISK AND COST**. Additional expenditure incurred shall be recovered from your firm. Undertaking certificate in this regard **on firm letterhead** should submit during technical bid. In this regard, a certificate as per **Appendix 'J'** attached shall be submitted.

3. **Commercial Bid.** The price will be quoted strictly for all **Scope of Supply** as per Specification document (including indicative drawings) attached in the bid (The same is attached to this document as well). The rate shall also be deemed to include all charges like GST, labour charges Excise, design vetting, soil testing, Sales, transportation cost (including loading/ unloading charges), taxes, VAT, freight, insurance during transportation, etc for supply of stores, civil and electrical items. This office will not accept any additional liabilities on this account.

4. **Delivery Period (Completion Period).** Delivery (Completion) period for **Supply of stores** as per scope of technical specifications attached herewith would be **60 days** from the effective date of placing SO on GeM Portal. Extension of contracted delivery period will be at the sole discretion of Buyer, with applicability of LD clause, in accordance with provisions of DPM-2025 and its addendums.

5. **Site Visit.** The firm shall inspect the proposed site of work by making prior intimation to acquaint themselves with regard to the nature and conditions of site, nature and means of local communication, working hours, conditions of site and all other cognate matters concerning the supply of the store until the construction site. Any Paths, tracks, approaches etc required for the movement of plants, equipment, machine etc to the work site required for the same will be responsibility of the firm. A certificate of site visit on the alongwith the geo tagged photograph /certificate signed by user unit rep & rep of 121 Engineer Regiment regarding site visit must be attached with the tech bid documents.

6. **Design and Drawings.** The L1 Bidder will get the Structural, Architectural and Foundation designs (as per the site) vetted by any of the IITs/NITs institute with seal in original and will submit in form of an ink signed copy. Vetted design will be submitted within 15 days from the date of placement of supply order prior to commencement of **Supply of Large Store Shelter**. All designs must confirm to applicable standards and regulations and shall undergo third party vetting prior to approval. L1 bidder will be whole and sole responsible for the third party vetting of the designs.
7. If any discrepancies or required modification in Architectural/Structural/ Service design/ drawings shall be rectified by the bidder at no additional cost.
8. **User Manual.** L1 bidder shall be responsible for furnishing a detailed user manual for the **Large Store Shelter structure**, including structural and architectural design details, nomenclature of components, Layout drawings of electrical, fire extinguisher, lightening conductor, earthing, and fire alarm system. The user manual to be printed and submitted in both hard & soft copies.
9. **Defect liability /Warranty.** A certificate regarding defect liability of stores is required to be submitted by the vendor on completion of supply of the job. The minimum defect liability period for this job is 2 years.
10. **Litigation/ Arbitration.** The timely completion of all supply of stores as per scope of the supply order by the vendor is of paramount importance for operational reasons and time constraints. Hence, no time extension of any kind shall be granted, except under Force Majeure Conditions. No litigation or arbitration under any circumstances at any stage shall be applicable. The decision of Chief Engineer, Headquarters 4 Corps Engineers Branch shall be final and binding in all matters. **Vendors not willing for this pre-condition are advised not to participate in the tendering process.**
11. **Probable Date of Completion (PDC).** The supply of complete stores under this contract shall be completed by 60 days from the date of contract.
12. **Performance Bank Guarantee (BG).** Performance Bank Guarantee upto 5 % of the total cost of supply order shall be deposited by the vendor in the form of Bank guarantee, from a scheduled bank, in favour of **Commanding Officer, 121 Engineer Regiment** within **15 days of the issue of the supply order**. The Bank guarantee shall be released to the vendor after two year of completion of Job.

NON DISCLOSURE CERTIFICATE

I / We M/s _____ certify that all documents / drawing / specification shall remain confidential and will be disseminated restrictively for the sole purpose of executing the job. I / We also certify that we have been made a acquainted with the provision of Indian Official Secret Act-1923 and I / We will be liable in case of breach of official trust to the penalties detailed in the Act.

Place:

(Name of Signatory in Block letters)

Date:

(Complete address of the firm
and Firm's seal)

TENDER CONDITIONS ACCEPTANCE LETTER

(To be given on Company Letter Pad)

Date:

To,

SUBJECT: ACCEPTANCE OF TERMS AND CONDITIONS OF TENDER

Tender Reference No. _____

Name of Tender Work: _____

Dear Sir,

1. I/We have downloaded/obtained the tender documents for the above mentioned Tender / Work from the website namely _____ as per your advertisement given in the above mentioned website.
2. I/We hereby certify that I/We have read entire and conditions of the tender documents from Page No _____ to _____ (including all documents like annexure (s) , schedule (s) etc, which form part of the contract agreement and I/We shall abide hereby the terms / conditions / clauses contained therein.
3. The corrigendum issued from time to time by your department/organisation too have also been taken into consideration, while submitting this acceptance letter.
4. I/We hereby unconditionally accept the tender condition of above mentioned tender documents or corrigendum in its totally/entirely.
5. Technical Bid and its enclosures (scanned copy of all pages of technical specifications including all enclosures and drawings duly stamped and ink signed on each page) as uploaded on the GeM Portal.
6. In case any provisions of this tender are found violated, your department/organization shall be at liberty to reject this tender/bid including the forfeiture of the full said **Bank Guarantee** absolutely and we shall not have any claim against department in satisfaction of this condition.

Enclosures: (As per Paragraph 5 above)

Place:

(Name of Signatory in Block letters)

Date:

(Complete address of the firm and Firm's seal)

BID SECURITY DECLARATION CERTIFICATE

I / We, M/s..... hereby certify that I /We have read entire terms and conditions of the tender documents (including all documents like annexures, schedules, etc, which form part of the tender and I / We shall abide hereby the terms /conditions /clause of technical specification contained therein. I / We, M/s_____ hereby also declare that I / We will not modify or withdraw my bid during the bid validity. If I/We withdraw or modify bid during the bid validity, I / We will be liable to be blacklisted /banned / suspended for a period of one or more years.

Place:

Date:

(Name of Signatory in Block letters)
(Complete address of the firm
and Firm's seal

AFFIDAVIT FOR SUBMISSION OF ORIGINAL/GENUINE/UNTAMPERED DOCUMENTS

I / We, M/s..... hereby certify that any editing / tampering to any certificates / documents, Terms and Conditions, Technical Specification or submission of any forged /fake documents while technical bid submission, will lead to rejection of my bid and I/We will be suspended for a period of one year. I / We will also become liable for penal actions as per directions of higher HQ and I/We will be treated as technically disqualified. I/we further declare that I/we will not represent against such rejection.

Place:

Date:

(Name of Signatory in Block letters)

(Complete address of the firm
and Firm's seal)

Note- Appendix D to be submitted as affidavit on non-judicial stamp paper or e-stamp paper duly notarized.

Appendix 'E'

CONTRACT ASSURANCE CERTIFICATE

I / We..... hereby declare that supply of stores of **Three (03) x Large Store Shelter** as per technical specification and quantity in tender will be carried out by or before the last date of completion, if I/we fail to do so, Commanding Officer 121 Engineer Regiment may cancel my/our contract/supply order. I/we further declare that I/we will not represent against the cancellation of contract/ supply order.

Place:

Date:

(Name of Signatory in Block letters)
(Complete address of the firm
and Firm's seal)

AFFIDAVIT REGARDING NOT BLACKLISTED / BANNED

It is certified that M/s_____ has not been **blacklisted / banned** in last 3 years financial years from any Central /State Govt Department & no **LD charges** has been imposed on my firm in last 3 financial years. It is also declared that no **show cause notice /Final notice** for any job has been furnished by the user unit in past 3 financial year. At any stage of tender, if this declaration is found to be false then bid/ Supply order may be rejected or cancelled. M/s_____ will not represent against the rejection/cancellation of bid / supply order.

Place:

(Name of Signatory in Block letters)
(Complete address of the firm
and Firm's seal)

Date:

Note- Appendix F to be submitted as affidavit on non-judicial stamp paper or e-stamp paper duly notarized.

UNDER TAKING CERTIFICATE

I / Wehereby declare that we have visited the store dumping /construction site for the assessment of the connectivity and transportation condition before participating in this tender. Geo-tagged photographs/user signed certificate is attached with the certificate as proof of the same.

Place:

Date:

(Name of Signatory in Block letters)
(Complete address of the firm
and Firm's seal)

Signature of Rep of User Unit

Signature of Rep of 121 Engr Regt

Annexure to Appx 'G' to site visit

GEO TAGGED PHOTOGRAPHS OF SITE VISIT ON XX-XX-XXXX

Note- Photograph to include the proprietor of the firm, user unit rep and 121 Engr Regt rep.

UNDERTAKING CERTIFICATE

I/ We hereby declare that I/ We will accommodate the suggested changes as per functional requirement of user during the course of project.

Place:	(Name of Signatory in Block letters)
Date:	(Complete address of the firm and Firm's seal)

**UNDERTAKING CERTIFICATE FOR TERMINATION/CANCELLATION
OF WORK ORDER**

1. It is certified that this firm M/s_____ has agreed the following terms and conditions against work progress on supply of the said job which fails Commanding Officer, 121 Engineer Regiment shall have the **right to cancel the supply order** and purchase the stores at our firm's **RISK AND COST**. Additional expenditure incurred shall be recovered from our firm: -

1.1 Supply not started within 01 month (30 days) after issuing work order.

1.2 Overall 50% of stores not delivered within 45 days after issuing of supply order.

Place:

(Name of the proprioter)
(With seal and signature)

Date:

PART-II

TECHNICAL SPECIFICATIONS FOR LARGE STORAGE SHELTER (18.30M X 6.1M X 4.75M HEIGHT) WITH 1.5 M VERANDAH)

1. Storage Shelter (18.30M x 6.1M x 4.75M Height) with 1.5m Verandah.

Pre-fabricated Rectangular Hollow Sections (RHS) of size 18.30m x 6.1m x 4.75m height with 1.5m verandah on one side with tubes to conform to IS – 4923-1997 grade Yst 240. The structure shall have dimensions as per the drawings No CE, 4 Corps/NON PUF/LSS (18.30M)/2017-18 having three sheets from sheet No 1/3 to 3/3 attached. The wall and roof shall be made up of using 0.80mm PPGI trapezoidal sheet fixed using STSD screws on to the steel framework. The structure shall be fabricated on a prepared plinth for Seismic Zone V, Wind Speed of 55m/s (As per IS 875) and temperature range of -20 to + 50 degree C.

2. Design Criteria. The structure shall conform to IS 2062 and fabricated on the basis of parameter as given under.

(a)	Seismic	-	As applicable for seismic Zone V
(b)	Snow load	-	1.5 m standing on roof
(c)	Live loads	-	120-150 Kg/Sqm
(d)	Wind speed	-	55 m/s (As per IS-875)
(e)	Temperature	-	(-) 40 ⁰ to (+) 50 ⁰
(f)	Length	-	18 .30 m
(g)	Width	-	6.1m
(h)	Height(Ridge)	-	4.75 m

(j) The shelter shall be made of pre-fabricated steel structure conforming to IS 4923 of 1992 and IS 2062 of 1984.

(k) Roof covering shall be provided with PPGI sheets of 0.80 mm. The roof truss shall be designed for 1.5 m standing snow load and roof slope shall be 1:2.

3. The structure shall consist of steel RHS conforming to IS 4923 of 1997 grade Yst 240 & as per drawings attached. Main shelter column of size 122mm x 61mm x 3.6 mm shall be provided at 2.6 m centre to centre distance. The column bottom end plate of size 170 mm x 220 mm x 6mm shall be fixed to concrete flooring using foundation bolts. The column shall also have top plate of size 150 mm x 200mm x 6mm for connection with truss plate. The verandah column are made using RHS of 80mm x 40mm x 3.2 mm. The trusses are made of using RHS section of 80 x 40mm x 3.2mm at top and bottom cord of truss and 50mm x 25mm x 2.9 mm thick internal members. Split trusses shall be joined using connection plate of 6mm thick with nuts & bolts. Purlin shall be made of RHS of size 96mm x 48mm x 3.2 mm and shall be fixed between trusses with suitable cleats and nuts & bolts. Horizontal Runners made of 80mm x 40mm x 3.2mm RHS shall be fixed to the column.

4. All steel items shall be procured from main manufacturers e.g. SAIL / JSW / TATA STEEL / ESSAR conforming to relevant IS specification and all accessories shall be ISI marked.

5. PPGI Sheet Specification. Thickness of walls & roofing sheet shall be 0.80 mm with guard film. The PPGI sheet shall have minimum coating of 4-5 micron epoxy primer and 18-20 micron polyester topcoat. The top of PPGI shall have a Guard film of 30-40 micron on the finished surface only for protection against-scratches during handling and transportation. The backside of PPGI shall have 5-8 micron primer. The pre coated GI sheet should conform to IS-14246-1995 with manufacture test certificates conforming for the above specification. Base metal of PPGI shall be of CRCA as per IS-513 & Galvanizing of 120gsm as per IS-277 . Make Uni Fix / Jindal metec or equivalent brand with IS specification.:-

(a) The inside and outside colour of wall sheet & roofing sheet will be approved by accepting officer / Engineer in charge. The L1 vendor should submit the sample colour to the Accepting Officer within 15 days of placing of the supply order for the final approval. Clarification if any will be referred to Accepting Officer, choice of Accepting Officer is deemed final.

(b) The colour of flashing shall match the overall colour scheme

6. Finish. All steel work shall be given two coat of anti corrosive red oxide zinc chromate primer and one coat of synthetic enamel Paint (Make Berger / Nerolac / Asian) by the manufacturer in the factory. Thereafter, one coat of synthetic enamel Paint shall be applied at site on prepainted surface (Paint of 20 ltr with thinner(qty as per appropriate mix) and two painting brush of size 4" to be supplied by the vendor).

7. Openings

(a) Steel Doors. Two numbers door of size 1000mm x 2030mm with outside opening shall be provided. The door frame shall be made in RHS section of 80x40x3.2mm fitted to the horizontal runners with the help of cleats & nut bolts. The door shutter shall be made with L angle all round & 1.25 mm thick ms sheet welded to the angle. The door shutter shall be fixed to the RHS frame with four numbers hinges. In addition, the door will have steel aldop 300mm long, two numbers Tower bolts of 200 mm & two numbers steel D type handle of 150mm length.

(b) Steel Windows. Seven numbers on front and back side wall and two windows on gable wall of double shutter window of size 1000 x 1000 mm with outside opening shall be provided. The window frame shall be made in RHS section of 80x40x3.2mm fitted to the horizontal runners with the help of cleats & nut bolts. The window shutter shall be made with L angle all round & 3 mm thick acrylic transparent sheet fixed to the angle with 10mm square beading. The window shutter shall be fixed to the RHS frame with four numbers hinges. In addition the window will have four numbers tower bolt of 100 mm, two numbers D type handles of 150 mm, two numbers peg stays MS grill of 8 mm square bar hollow shall be provided to all windows including fixing arrangements.

(c) Sunshades. Suitable sunshades made out of PPGI Sheets & angle iron frame of 35x35x3 mm and flat iron 35x3 mm shall be provided to all external windows . The minimum projection for the sunshades will be 450 mm and 300 mm wider than the width of the opening.

8. **Roofing.** The roof shall be provided with 0.80mm PPGI sheets fixed on to the framework of trusses and purlines using STSD screws with suitable washers. PPGI sheets shall be over-lapped with each other along with necessary flashing at the corners. The sheets shall be laid with a minimum 150 mm of side lap with the last profile overlapping. The roof shall have a minimum projection of 450 mm from the eaves walls and 300 mm at the gable end. Self-tapping self-drilling (STSD) screws are fixed on each ridge of PPGI sheets in all purlins of the roof. 0.80mm thick pre-coated plain sheet matching with the roof sheet of size 3.0m long and 0.60m wide ridge shall be Provided . All overlaps between sheets shall also be tightened using STSD screws. All the STSD screws should be fully tightened. The inside colour of roof shall be white and the outer colour shall be Bus Green / Camouflage Pattern shade No 0209 of Asian paints or equivalent in Nerolac / Berger. The inside and outside colour of wall sheet & roofing sheet will be approved by accepting officer / Engineer in charge. The L1 vendor should submit the sample colour to the Accepting Officer within 15 days of placing of the supply order for the final approval. Clarification if any will be referred to Accepting Officer, choice of Accepting Officer is deemed final.

9. **External Cladding.** The walls of the shelter shall be provided with 0.80 mm thick PPGI sheets fixed on to the framework steel columns and runners using STSD screws with suitable washers. PPGI sheet shall be over-lapped with each other along with necessary flashing at the corners. All overlaps between sheets shall also be tightened using STSD screws. All the STSD screws should be fully tightened. The inside and outside colour of wall sheet & roofing sheet will be approved by accepting officer / Engineer in charge. The L1 vendor should submit the sample colour to the Accepting Officer within 15 days of placing of the supply order for the final approval. Clarification if any will be referred to Accepting Officer, choice of Accepting Officer is deemed final.

10. **Glazing.** Windows shall be fully glazed with transparent acrylic sheet 3 mm thick. Sufficient number of glazing clips shall be provided.

11. **Foundation.** The following material shall be provided by the firm:-

(a) **Bolts.** Stanchion proposed shall have base plate, holding down high tensile strength bolts (0.45 meter long and 12 mm diameter) and nuts for embedding into concrete.

(b) **Base Plate.** 6 mm thickness.

(c) Template for casting of foundation bolts.


12. **Welding.** Proper welding joint shall be formed where specified as per the design. All welding works shall be continuous and butt-fillet type, as per IS: 823 – 1964 and IS: 816 – 1976.

13. **Nuts & Bolts.** Hexagonal bolts with nuts shall be fit tight with washers as per IS: 1363-1967. All nuts and bolts shall be of high tensile steel and galvanized using Zinc Black. 10% spare nuts, bolts and washers shall be provided per shelter. Fastening means shall be provided for the items to be fitted at the time of erection.


14. **Wind Tie** Four numbers of Wind tie shall be provided on both side Slopes of roof longitudinally with FI 40x4mm including adequate fixing arrangements for protection of PPGI sheets. The colour of wind tie should match with that of roof.

15. **Materials.** All materials required for manufacture of the shelter shall be new and shall comply with relevant bureau specifications and bear the mark.
16. **Minor Details.** Details not mentioned in the specifications but required as per sound and good engineering practice shall be provided by the supplier. Only superior specifications shall be accepted, after obtaining written clearance from the Chief Engineer HQ 4 corps.
17. 01 No RHS box 50 x 25 x 2.9 mm 2.55mm welded with 4 mm thick MS Sheet of size 80mm x 80mm with 4 Nos holes will be provided, for hanging of fans. 2 Nos of rubber washer of size 80mm and 4 Nos of nut and bolts 10 mm dia and 75 mm long will also be supplied with each runner with washer of suitable size.
18. **Rain Water Harvesting.** Eaves gutter shall be provided on front and side with PPGI Sheet, duly painted matching the roof colour. Galvanized class 3 (three) thickness of sheet shall be 0.80mm and 200 x 200 x 200mm. It shall be fixed to truss with adequate fixing arrangements. Both ends of eaves gutter should be sealed with PPGI sheet and one end shall be provided 3.0 m length and 110mm dia PVC pipe with necessary fixing accessories and fittings for water collection tank placed by user.
19. **User Manual .** L1 Vendor shall submit hard and soft copy of the user manual to include the store list, photographs of parts for easy identification and drawings along with connected literature to the Accepting Officer within 15 days of placing the supply order and to the paying authorities at the time of delivery.

DESIGN : LARGE STORAGE SHELTER (18.33M X 6.1M X 4.75M HEIGHT) WITH 1.5M VERANDAH) (LSS)

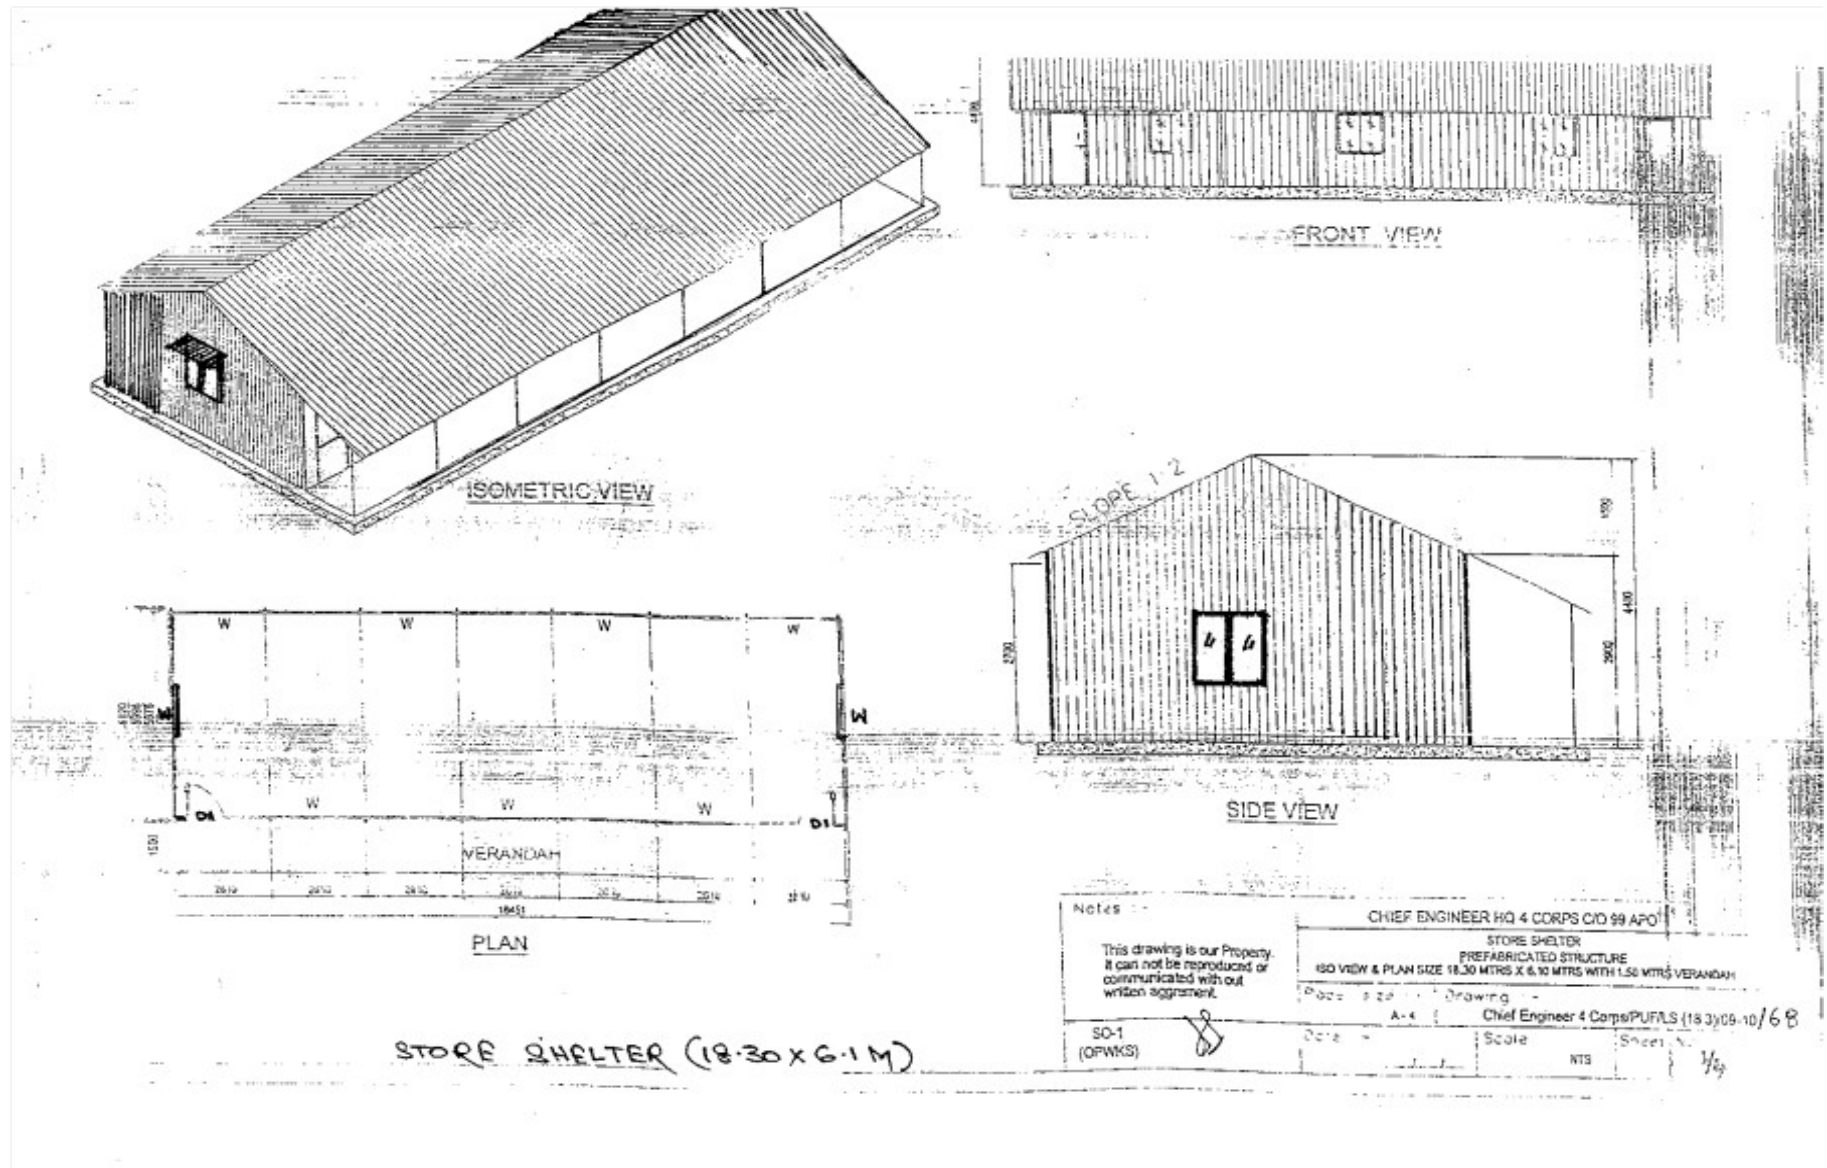

LARGE STORAGE SHELTER (18.33M X 6.1M X 4.75M HEIGHT) WITH 1.5M VERANDAH) (LSS)

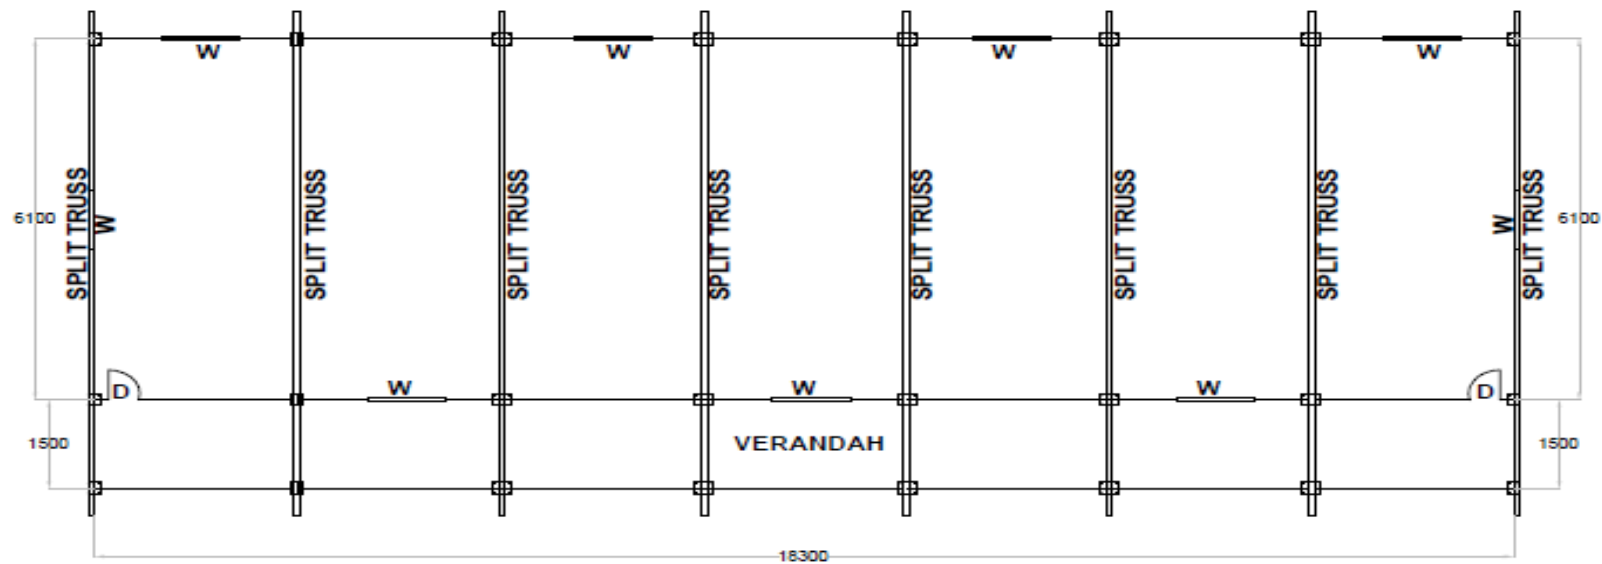


**LAYOUT PLAN
STORE SHELTER 18.30 X 6.10 MTR**

CHIEF ENGINEER HQ 4 CORPS

Drg Name	LARGE STORE SHELTER 18.30 X 6.10 MTR	
DRG NO:	CE 4 CORPS/NON PUF/LSS(18.30M) /2017-18	
Approved by		
Date:-	SCALE NTS	SHEET 2/3

LARGE STORAGE SHELTER (18.33M X 6.1M X 4.75M HEIGHT) WITH 1.5M VERANDAH) (LSS)

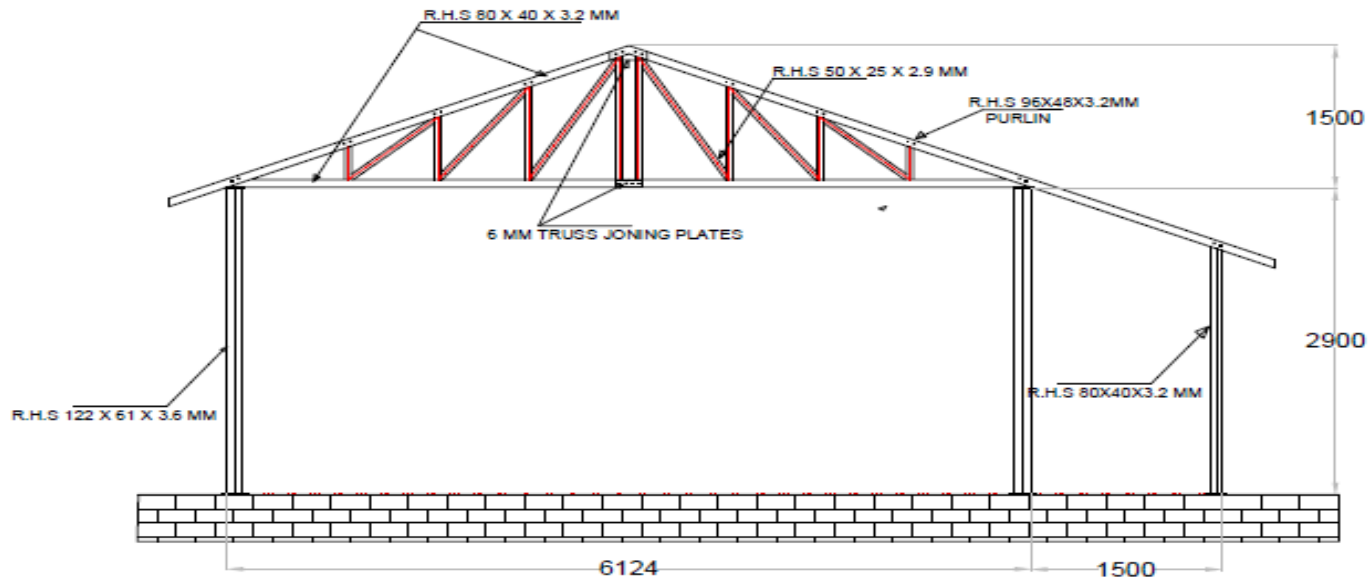

TRUSS PLAN
STORE SHELTER 18.30 X 6.1 MTR

CHIEF ENGINEER HQ 4 CORPS

Drg Name	LARGE STORE SHELTER 18.30 X 6.10 MTR	
DRG NO:	CE 4 CORPS/NON PUF/LSS(18.30M) /2017-18	
Approved by		
Date:-	SCALE NTS	SHEET 1/3

STORE LIST OF LARGE STORE SHELTER
JOB NO : OT/EC/4/5/26-27/2447

Ser No	Nomenclature of items	A/U	Qty for 01 x shelter	Qty for 03 x Shelter
1	Superstructure of Large Store Shelter (LSS) of size 18.30 M x 6.10 M x 4.75 M height with 1.50 M verandah as per CE, HQ 4 Corps drawing No CE 4 Corps/NON PUF/ LSS(18.30M)/2017-18, Sheet No 1/3 to 3/3.	Nos	01	03
Construction Material.				
2	Cement OPC 43 Grade packed in HDPE bag each 50 Kg wt conforming to IS 8112 - 1989 (Make:- Birla Gold / Ambuja / Ultratech / ACC / JK / Dalmia)	Bags	225	675
3	Coarse Sand free from vegetation	Cum	26	78
4	Coarse aggregate 20mm graded	Cum	9	27
5	Coarse aggregate 40mm graded	Cum	19	57
6	Coarse Aggregate 40-63mm graded	Cum	20	60
7	RR Stone Masonry	Cum	29	87
8	Water Proofing Compound Conform to IS 2645-2003. (Make:- Pidilite / Dr Fixit / Fevicol).	Kgs	17	51
9	Mild Steel bars of size 6 to 8mm dia Conform to IS 432 (Part 1) 1982 Make:- TATA / SAIL / JSW)	Kg	60	180
10	Mild Steel bars of size 10mm dia and above Conforming to IS 432 (Part 1) 1982 (Make:- TATA / SAIL / JSW)	Kg	61	183
11	Glass dividing strips 30 x 4mm (Make :- Prayag / Saint Gobin / Modi Guard)	RM	167	501
12	MS Binding wire	Kg	2	06
E/M Items				
13	Distribution box 8 way SPN, 240 volts copper bus bar and neutral link earthing stud conforming to IS-13032 & IS – 8623 double door type. ((Make : (Havells/Finolex/Polycab/ Natural white or equivalent)	Nos	1	03
14	MCB SPN 240 Volts 32 Amps(Make : (Havells/Finolex/Polycab/ Natural white or equivalent)	Nos	1	03
15	MCB SP 6 to 32 Amps (Make : (Havells/Finolex/Polycab/ Natural white or equivalent)	Nos	6	18
16	PVC tape 19mm wide 5 m long (Make : (Havells/Finolex/Polycab/ Natural white or equivalent)	Nos	2	06
17	Cable PVC insulated electric cables (heavy duty) 1100 volts grade multi stranded copper conductor of size 1.5 Sqmm single core (FRLS) confirming to IS 1554 (part-1) 1988 (Make : (Havells/Finolex/Polycab/ Natural white or equivalent)	RM	470	1410
18	Cable PVC insulated electric cables (heavy duty) 1100 volts grade multi stranded copper conductor of size 2.5 Sqmm single core (FRLS) confirming to IS 1554 (part-1) 1988 (Make : (Havells/Finolex/Polycab/ Natural white or equivalent)	RM	370	1110

Ser No	Nomenclature of items	A/U	Qty for 01 x shelter	Qty for 03 x Shelter
19	PVC casing capping of size 1" Medium Grade (snow white) (Make : (Havells/Finolex/Polycab/ Natural white or equivalent)	RM	70	210
20	PVC casing capping of size 3/4" Medium Grade (snow white) (Make : (Havells/Finolex/Polycab/ Natural white or equivalent)	RM	50	150
21	Switch Piano 5 Amp 230 Volts Flush type one way (snow white) (Make : (Havells/Finolex/Polycab/ Natural white or equivalent)	Nos	16	48
22	LED Tube light fittings 20W rechargeable 230V box type 4 feet with CRCA body Pre coated white and Prewired for LED tube complete (Make : HAVELLS/BAJAJ/PHILIPS/CROMPTON)	Nos	13	39
23	Steel screw full thread with rawl plug 1 1/2" size (ISI Marked) 100 Nos Pkt	Pkt	4	12
24	PVC switch board (snow white) size 7"x4" for sockets and switches (Make : (Havells/Finolex/Polycab/ Natural white or equivalent)	Nos	10	30
25	PVC switch board (snow white) size 8" x 10" for main switches / DB (Make : (Havells/Finolex/Polycab/ Natural white or equivalent)	Nos	2	06
26	PVC 'L' bend and 'T' junction joint for PVC casing and capping conforming to IS 3419 (Part 3) (Make : (Havells/Finolex/Polycab/ Natural white or equivalent)	Nos	20	60
27	Switch socket combination(snow white) multipurpose 2 in 1, 15 Amp 230 Volts (Make : (Havells/Finolex/Polycab/ Natural white or equivalent)	Nos	2	06
28	Switch socket combination (snow white) 5 Amp 230 Volts (Make : (Havells/Finolex/Polycab/ Natural white or equivalent)	Nos	2	06
29	Service bracket 40mm dia GI Tubing medium grade 1.5 Mtr Long (Make : (Havells/Finolex/Polycab/ Natural white or equivalent)	Nos	1	03
30	Service cable PVC insulated aluminium conductor, 1100 volt grade Heavy duty served with inner sheathing of PVC tap and overall PVC sheathed in service connection 10 Sqmm 2 (Make : (Havells/Finolex/Polycab/ Natural white or equivalent)	RM	100	300
31	Ceiling Rose three terminal (snow white) (Make : Anchor/ SSK/CONA)	Nos	16	48
32	LED Bulk head fitting high pressure die cast aluminum front cover with glass cover with specially design gasket with LED lamp 10 watts rechargeable (Make : HAVELLS/BAJAJ/PHILIPS/ CROMPTON)	Nos	3	09
33	PVC Flexible wire copper conductor multi stranded 0.0016/76 (Make : (Havells/Finolex/Polycab/ Natural white or equivalent)	RM	12	36
34	PVC Flexible Conduit pipe 15 mm dia (Make : (Havells/Finolex/Polycab/ Natural white or equivalent)	RM	9	27
35	PVC Round/Squire Block (Make : (Havells/Finolex / Polycab / Natural white or equivalent)	Nos	16	48
36	Fire extinguisher of one kilogram capacity, dry power type conforming to IS-13849 along with its accessories (Make: Cease fire/Omex/Alfa Fire)	Nos	4	12

Ser No	Nomenclature of items	A/U	Qty for 01 x shelter	Qty for 03 x Shelter
37	Earthing plate 600 x 600 x 6 mm Galvanised steel suitable for GI strip fittings, drilled with 2 Nos holes for 6 mm dia near one side.	Nos	1	03
38	CI earth pit cover of size 300 x 300 x 6 mm with Angle iron of size 20x20mm, 3 mm thick with MS frame.	Nos	1	03
39	Funnel fitted with 20 mm diameter GI Pipe 1.5 m Long. Pipe (Make:-Jindal/Tata/Kalinga)	Nos	1	03
40	GI wire 4 mm diameter (For earthing).	RM	15	45
41	Charcoal	Kg	75	225
42	Salt normal	Kg	75	225
43	Air termination single pointed aluminium rod 12 mm dia and 300 mm long.	Nos	2	06
44	Testing point terminal block make of gun metal & phosphorus bronze size 75 x 75 x 25 mm drilled and screwed including 3 Nos 8 mm dia 25 mm long hexagonal head screw	Nos	2	06
45	Aluminium strips 25 x 3.0 mm	RM	20	60
46	Galvanised Iron strip 32 x 6 mm	RM	15	45
47	Funnel fitted with 20 mm diameter GI Pipe 1.5 m Long. Pipe (Make:-Jindal/Tata/Kalinga)	Nos	2	06
48	Earthing plate 600 x 600 x 6 mm Galvanised steel suitable for GI strip fittings, drilled with 2 Nos holes for 6 mm dia near one side.	Nos	2	06
49	CI earth pit cover of size 300 x 300 x 6 mm with Angle iron of size 20x20mm, 3 mm thick with MS frame.	Nos	2	06
50	Insulating PVC block 75x75x30 mm with insulating clamp nut and bolt (Make:-Presto/Polycab/Finolex)	Nos	20	60
51	Study chair of size length 56 Cm, Height 82 Cm and Width 56 Cm, Type : Lacquered finish with arm, seat and back cushion, velvet upholstery (Make :- Supreme or equivalent)	Nos	1	03
52	Study Table of size 4' X 2', Wooden top on round tube structure with three drawers on one side.	Nos	1	03
53	Steel almirah of size 1855mm with 4 shelves. MS sheet doors and and locker 1.00mm thick, lock material brass and steel finished and thickness of shelves 0.90mm	Nos	4	12
54	Mild Steel rack adjustable ,sheet 1.00mm thick, nuts and bolts are in hexagon blk steel, overall height 1.755m depth 0.410m and width 0.915m	Nos	8	24
55	Hand Held Trolley of size 1200 x 900 x 1200 mm of 2 mm thick MS platform and size of wheel 127 mm with loading capacity minimum 200 kg and overall weight of trolleys 19 Kg.	Nos	2	06

Ser No	Nomenclature of Items	A/U	Qty
Tool List			
56	Kassi with handle (Make:-SAIL/TATA/Jindal)	Nos	1
57	Black Steel SR Shovel Spade Belcha (Make:-SAIL/TATA/Jindal)	Nos	1
58	Plaster trowel with wooden handle ISI Markded (Make:-SAIL/TATA/Jindal)	Nos	1
59	Showel Square Nose 14 Gauge blade size 310 x 245 mm, shaft size 710 mm fitted with strong Steel crutched wooden handles. (Make:-SAIL/TATA/Jindal)	Nos	1
60	Plumb Bob Iron, best quality ISI Marked	Nos	1
61	Crow Bar 1.5" dia 4' long (Make:-SAIL/TATA/Jindal)	Nos	1
62	Hammer 1 Kg with Wooden Handle (Durmut) (Make:-Taparia/Venus/JK)	Nos	1
63	Hammer 0.5 Kg with Wooden Handle (Durmut) (Make:-Taparia/Venus/JK)	Nos	1
64	Brick Line 30 Mtr (Nylon Dhaga)	Nos	1
65	Traveler Brick Mason 4" 305mm (Make:Taparia/ Venus/Miranda)	Nos	1
66	Sprit Level (Make:- Venus/Bosch/Taparia)	Nos	1
67	Measuring tape 30Mtr Steel, (Make :- Freeman/Venus/JK)	Nos	1
68	Water bucket steel 13" dia Make TATA/ HIRA/ TAPARIA or equivalent.	Nos	1
69	Picks Axes with Chisel and Point Ends (Kudali 14 CP) nominal weight 3.0 Kg, overall length (minimum) 595mm with handle, Make : Taparia/Tata/Hira	Nos	1
70	Lime Brush Best quality	Nos	1
71	Painting Bursh 100 mm best quality ISI Marked	Nos	1
72	Hacksaw frame large with blade 05 Nos (Make : Taparia/Tata/Hira)	Nos	1
73	Galvannised iron Pan Mortar (Tasla), 18 Gauge, 20" dia minimum weight 2 Kg (Make : Tabaria/Tata)	Nos	3
74	Wooden Waterproof Plywood, Thickness 12mm	Sq m	3
75	Nails various sizes	Kg	1
76	Rammer Earth with Handle (Minimum Wight 5 Kg without handle) Make : Taparia/TATA (Agro)	Nos	1
77	Tester for Electrician with plastic handle 150mm make BOSCH/Taparia/Jhalan/HIRA/TATA	Nos	1
78	Electric Drill Machine heavy duty 500 watt electrical backup with battery and charger etc with one set pf drill bit of size (4mm, 6mm and 8mm wood and stone each) Make : BOSH/TAPARIA/HIRA	Nos	1
79	Drill bits HSS 5mm, 8mm & 10mm dia for electric drill machine (Make : Mrinida/Hilit/Black & Decker)	Set	1
80	Electric tile cutting machine with interchangeable biades (20 Nos) Make "Bosh/Taparia/Jhalan/Hira/TATA	Nos	1
81	Electrical Sheet cutter machine with blade (20 Nos) Make : BOSH/Tapaira	Nos	1
82	PUF Rivet Machine Make : BOSH/TAPARIA/HIRA	Nos	1
83	Centre punch 8mm dia best quality	Nos	1
84	Pluming Tool kit Make : Bosh/Tapaira (To be provide As per requirement of Plumber) (a) Pipe Wrich (b) Haksaw (c) Haksaw frame blade (d) Wice (e) Screw driver (f) Cutting Player (g) PPR PVC Pipe cutter (h) Universal pipe wrinch (j) PPR pipe welding machine	Nos	1
85	Water level pipe 30 mtr long Superior	Nos	1

PART- III

ORGANISATION SPECIFIC TERMS AND CONDITIONS

1. **Supply Location.** The **Supply of Three (03) x Large Store Shelter** is required in **Gen Nakyo GG, Arunachal Pradesh**. Any vendor/ firm having queries regarding the same are advised to take prior appointment with the **Commanding Officer, 121 Engineer Regiment**. Correspondence regarding same may be carried out on **work-123@gov.in**.

2. **Submission of Documents.** Interested bidders shall submit the bids along with all requisite documents on GeM Portal as per fixed timelines. If any bidder fails to submit any of the documents as mentioned in this Paragraph, under suitable heads on GeM, his bid will be considered as REJECTED.

2.1. **Technical Bid.** Scanned copy of the following documents are mandatory and will be uploaded online:-

2.1.1 Bid document with Stamp and Sign of the firm.

2.1.2. Plan/ Technical drawings with stamp and signature of bidder.

2.1.3. Corrigendum (if issued) with stamp and signature of bidder.

2.1.4 Bid Conditions Acceptance Certificate.

2.1.5. Certificate of acceptance of terms and conditions of Bid on firm's letter head (Scanned and uploaded). The bidder shall certify for acceptance of all tender conditions of online Bid and furnish a certificate regarding the same. The certificate duly signed shall be scanned and uploaded. In case of any deviations, the bid shall be rejected. If the certificate is signed by legally authorized signatory, a copy of the authorization letter needs to be enclosed/ uploaded.

2.1.6. The Bid Security/ **Earnest Money Deposit (EMD) 3%** as applicable shall be submitted on GeM prior to bid submission closing date. If the EMD is not received as mentioned, then the bid will be **REJECTED**.

2.1.7. Scanned copy of GST registration certificate. If bidder does not submit the GST registration certificate, the bid will be rejected.

2.1.8. TIN Number / PAN Number/ Certificate.

2.1.9. ECS and mandate form and Blank Crossed cheque.

2.1.10. Certificate for acceptance of terms and conditions of tender enquiry.

2.1.11. Certificate for Non-disclosure of Contract Documents.

2.1.12. ISO Quality Management System certificate (ISO 9001:2015).

2.1.13. ISO Environmental Management System Certificate (ISO 14001: 2015).

2.1.14. ISO occupational health and safety management system certificate (ISO: 45001: 2018).

2.1.15. Last three years income tax return verification.

2.1.16. Audited balance sheet of Last 3 (three) years.

2.1.17. Details of clients to which vendor has executed similar project in last five years with copy of proof (Supply order / Contract agreement, CRAC certificate, Completion Certificate and performance certificate).

2.1.18. Schedule of Requirement (SOR)/ Technical specification including clause by clause compliance of specification mentioned in ATC for evaluation by TEC.

2.1.19. ATC duly stamped and signed in each page by the authorized person of the firm concerned.

2.1.20. Affidavit regarding firm is not bankruptcy, litigation/ arbitration to be upload by the participant bidder.

2.1.21 The bidder must submit a valid latest **Solvency Certificate** issued by a National Bank (within last 6 Months) covering 50% of the tender value.

2.1.22. Assurance certificate from the bidder to complete the project within stipulated time period fixed by the consignee.

2.1.23. MII certificate as per criteria fixed by the buyer.

2.1.24. Warranty certificate for the asset for 2 years from the date of completion.

2.1.25. List of work in hand under progress as on date of submission of bid in firm letter head alongwith copy of work order/ supply order must be uploaded by the bidder.

2.1.26. **Performance.** Firms who have executed supply & construction of similar nature of work will be preferred in the High Altitude Area as mentioned in the work location (Refer Para 1 of this ATC). Firms not submitting their performance statement of last 5 years would be treated as disqualified and be rejected.

2.1.27. Any editing / tampering to any certificates/ documents, Terms and Conditions, Technical Specifications or any part of the tender while submission of bids; will lead to rejection of bid. Such bidder/ vendor will become liable for penal actions as per directions of higher Headquarters.

2.2 **Commercial Bid.** The price will be quoted strictly for all Scope of Work as per Specification document (including indicative drawings) attached in the bid (The same is attached to this document as well). The rate so quoted shall be deemed to include the provisions for all materials, stores, labour, design costs, laboratory set up, tests to be conducted, process, operations and requirements detailed in particular specifications irrespective of whether these appear as specific items or not in the Scope of Work. The rate shall also be deemed to include all charges like GST, Excise, Sales, transportation cost (including loading/ unloading charges), taxes, VAT, freight, insurance during transportation, etc for supply of stores, civil and electrical items. This office will not accept any additional liabilities on this account.

3. Test certificates to be submitted by contractor of all items for which applicable.

4. **Litigation/ Arbitration.** The timely completion of all works as per scope of the supply order by the vendor is of paramount importance for operational reasons. Hence, no time extension of any kind shall be granted, except under Force Majeure Conditions. No litigation or arbitration under any circumstances at any stage shall be applicable. The decision of Chief Engineer, Headquarters 4 Corps Engineers Branch shall be final and binding in all matters. Vendors not willing for this pre-condition are advised not to participate in the tendering process.

5. **Probable Date of Completion (PDC).** The supply of complete stores under this contract shall be completed by 60 days from the date of contract.

6. Additional Pre- Qualification Criteria.

6.1. Also, vendor/ OEM must have required machinery to deliver the complete requirement within stipulated time.

6.2. Vendor/ OEM to have a minimum annual turnover for past three (3) financial years must be more than 50% on total tender value or above.

6.3. Vendor should accommodate the suggested changes as per functional requirement of user during the course of project. A certificate confirming to his clause shall be provided by the vendor during bidding.

7. Consignee Details.

Commanding Officer,
121 Engineer Regiment.
PIN - 914121 c/o 99APO

8. **Payment.** 100% payment of the cost of the supply order can be made immediately after complete stores delivered including deposition of BG (as per Para 15 of Part 1), all concerned certificate and received in fit for use condition by the consignee / his authorized representatives after having checked and certified quality and quantity. **Commanding Officer, 121 Engineer Regiment** reserves the right not to accept the suppliers after stipulated delivery period and cancel Supply order for balance quantity. Decision of **Commanding Officer, 121 Engineer Regiment** will be final and binding in this regard. Bill in triplicate original copy duly stamped & pre-receipted will be submitted to consignee's unit for audit verification & payment. Original copy of supply order and amendment if only will be attached with the bill. In case of dispute of any nature concerning supply & payment the decision of Commanding Officer, 121 Engineer Regiment will be final & binding. **Payment will be made on completion of supply of store & after they have been inspected & approved by the Board of Officers.**

9. **Penalty.** In the event of breach of agreement on any account or non-supply of material, Accepting Officer, i.e. **Commanding Officer, 121 Engineer Regiment** shall have the right to cancel supply order and purchase the stores at the risk and cost of original supplier. Additional expenditure incurred on this account shall be recovered from the firm. If the supplier fails to supply the stores as per schedule of supply, a penalty rate of ½% (Half Percent) of the value of default per week or part thereof will be imposed upto a max of 10% (Ten Percent). If the delivery of stores by stipulated date is expected to be delayed, due to any cause beyond the control of the supplier, he will immediately on the happening of the event causing delay give notice in writing to **Commanding Officer, 121 Engineer Regiment** who after due consideration of circumstances, may grant reasonable time / extension for delivery of stores. The decision of **Commanding Officer, 121 Engineer Regiment** in this regard will be final and binding on the supplier / firm.

10. **Documents.** The following documents shall be prepared and submitted by the contractor to the paying authority alongwith the bill of making payment:-

10.1. Ink signed copy of invoice.

10.2. Guarantee/Warranty certificate (if applicable).

10.3. Copy of Performance Bank Guarantee.

10.4. Prescribed pre-stamped bills in triplicate.

11. **Payment Terms for Indigenous Contractors.** It will be mandatory for the Bidder to indicate their bank account numbers and other relevant e-payment details so that payments could be made through ECS/NEFT mechanism instead of payment through cheques. A copy of the model mandate form prescribed by RBI to be submitted by Bidders for receiving payments through ECS is at Form DPM-11 (Available in MoD website and can be given on request).

12. **Security Deposit (BG).** Upto 10% of the total cost of contact / supply order shall be deposited by the vendor in the form of Bank guarantee, from a scheduled bank, for a period of 26 months in favour of Commanding Officer, 121 Engineer Regiment within 15 days of the issue of the supply order.

13. **Subletting, Transfer, Assigning the Supply to Other Agencies.** The firm shall not sublet, transfer; assign the supplies of the items given in Schedule or any part thereof to any other firm. Any violation on this count shall render the offer/ supply order to be cancelled and the security deposit Performance Bank Guarantee forfeited. The prices quoted and accepted will be final and under no condition any increase in price shall be accepted.

14. **Delivery.**

14.1. Stores shall be delivered at construction sites at **Gen Area of Nakyo GG, Arunachal Pradesh** inclusive of packing forwarding and freight paid by road transport.

14.2. Supply shall be deemed complete when entire store delivery is physically inspected and duly received by consignee unit at the specified location.

14.3. Any items found not to conform to technical specification or defective due to any reason shall be rejected on receipt. Whatsoever, the same items shall be replaced by the vendor at site free of cost within a period of seven days of receipt of intimation from this office or unit concerned. On failure to do so, the Consignee will be at liberty to return the stores to the vendor at his risk and cost.

15. **Bank Details.** The details mentioned below will be filled by the firm before submission of quotations:-

15.1. Bank Name :

15.2. Branch Name :

15.3. Address :

15.4. Telephone No :

15.5. 9-Digit Code Number of the Bank & Branch appearing on the MICR cheque issued by the Bank.

15.6. Account type (S.B Account/Current account on cash credit) with IFSC & Branch code.

15.7. Ledger No/Ledger folio No.

15.8. Account number as appearing on the cheque book.

15.9 The following details in respect of tax will be filled by the firm :-

15.9.1. TIN with date of validity.

15.9.2. GST registration Number with date of validity.

16. **Risk & Cost.** In the event of failure on the part of vendor to supply the full quantity in the time stipulated or within any extended period granted by the accepting officer or in the event of failure to supply on any account, the accepting officer shall have the right to cancel the supply order and obtain the undelivered supplies from other sources at risk and cost of the vendor. The vendor is liable to pay the additional amount spent by the department in procuring of **Three (03) x Large Store Shelter** though a fresh supply order i.e., the defaulting vendor has to bear the excess cost incurred as compared with the amount contracted with the vendor.

17. **Force Majeure.** Should any Force Majeure circumstances arise, each of the contracting party shall be excused for the non-fulfilment or for the delayed fulfilment of any of its contractual obligations, if the affected party within 15 days of its occurrence informs the other party in writing. Force Majeure shall mean fires, floods, natural disasters or other acts, that are unanticipated or unforeseeable, and not brought about at the instance of the party claiming to be affected by such event, or which, if anticipated or foreseeable, could not be avoided or provided for, and which has caused the non-performance or delay in performance, such as war, turmoil, strikes, sabotage, explosions, quarantine restriction beyond the control of either party. A party claiming Force

Majeure shall exercise reasonable diligence to seek to overcome the Force Majeure event and to mitigate the effects thereof on the performance of its obligations under this contract.

18. Non-Disclosure of Supply Order Documents. Except with the written Consent of the Buyer, Seller shall not disclose the supply order or any provision, specifications, plan, design, pattern, sample or information thereof to any third party.

19. Litigation/ Arbitration. The timely Completion of the work as per scope of Technical sanction and supply order by the vendor is of paramount importance for Operational reasons. Hence, no time extension of any kind shall be granted except under natural calamities and unexpected circumstances. In case of non-adherence of delivery period the supply order would be cancelled at the sole discretion of the Chief Engineer, Headquarters 4 Corps Engineers Branch. No litigation or arbitration under any circumstances at any stage shall be applicable. The decision of Chief Engineer, Headquarters 4 Corps Engineers Branch shall be final and binding in all matters. Vendors not willing for this pre-condition are advised not to participate in the tendering process.

20. Rejection of Bids. Canvassing by the bidder in any form, and unsolicited letter, conditional quotations will result in rejection of the bid out rightly.

21. Tolerance Limit. Consignee reserves the right to increase or decrease 50% of the quantity of the required stores up to that limit without any change in terms and conditions and rates quoted by the vendor to take care of any change in the requirement during the period starting from issue of quotation till placement of supply order. While placing the supply order, the quantity ordered can be increased or decreased by the accepting officer within this tolerance limit.

22. Option Clause. Consignee reserves the right to place an additional 50% of the original supply ordered quantity in accordance with the same rates, terms and conditions of the present supply order within the currency of supply order.

23. Repeat Supply Order. Consignee reserves the right to place repeat Supply Order within 06 (Six) months from the date of successful completion of present supply order up to 50% quantity of items under the present supply order, rates, terms and conditions remain the same.

24. Miscellaneous.

24.1. Due to dynamic and urgent nature of operational works, maximum quantity (as laid out in quotation) may be ordered on L1 vendor by the means of part supply orders, before exercising option/repeat supply order clauses.

24.2. Manuals of relevant items will be handed over to the user.

Note. Any improvements/changes due to technological development carried out as per IS or Acts and norms of the State to above items/ work will be deemed to be included without any extra cost and intimate schedule changes to all concerned.

25. VAT, Excise and Sales Tax. Firm will ensure that all taxes including excise, VAT, sales tax and any other kind of taxes as applicable are paid at firm's end. This department will bear no liability for any dispute on this account.

26. Unwillingness to Quote. Bidders unwilling to quote should ensure that written intimation to this effect should reach before the due date and time of opening of the Bid, failing which the defaulting Bidder may be delisted/debarred for current financial year.

27. Fall Clause. The following fall clause will form part of the contract placed on successful bidder:-

27.1. The price charged for the supply and construction under the contract by the Contractor shall in no event exceed the lowest prices at which the Contractor supply and construction or offer to supply and construction of identical description to any persons/ organization including the purchaser or any department of the Central Government or any Department of State Government or any statutory undertaking the Central or State Government as the case may be during the period till

performance of all supply orders placed during the currency of the rate contract is completed.

27.2. If at any time, during tile said period the Contractor reduces the sale price, sells or offer to sell such stores to any person/ organization including the Accepting officer or any Department. of Central Government, or any Department or the Stale Government or any Statutory undertaking of the Centre or State Government as the case may be at a price lower than the price chargeable under the contract. He shall forthwith notify such reduction or sale or offer of sale to the Director General of Supplies & disposals and the price payable under the contract for the stores of such reduction of sale or offer of the sale shall stand correspondingly reduced The above stipulation will, however, not apply to:-

27.2.1 Exports by the Contractor,

27.2.2. Sale of good as original equipment at price lower than the price charged from normal replacement.

27.2.3. Sale of goods which have expiry dates.

27.2.4. Sale of goods at lower price on or after the date of completion of sale/ placement of the order of goods by the authority concerned under the existing or previous Rate Contracts as also under any previous contracts entered into with the Central or State Government Departments. Including their undertakings excluding joint sector companies and/or private parties and bodies

28. **Quality Assurance.** Contractor would provide the Standard Acceptance Test Procedure (ATP) within 01 month of the date of contract. Accepting officer reserves the right to modify the ATP. Contractor would be required to provide all test facilities at his premises for acceptance and inspection by Accepting officer. The details in this regard will be coordinated during the negotiation of the contract. The item should be of the latest manufacture, conforming to the current production standard and having 100% defined life at the time of delivery. **All the stores delivered will be subject to the acceptance by the Accepting Officer at site. The decision of the Accepting officer will be final & will be abide to.**

29. **Defect Liability Period.** The firm supplying of the **Three (03) x Large Store Shelter** would be responsible for any defect liability for a period of two year post completion of the Job. The vendor free of cost at consignee's site as early as possible/within shall replace any malfunctioning or defective items two weeks during with defect liability period.

30. **Security.** As the work is being exec in close proximity of IB/LAC, due to its confidentiality it is the responsibility of the vendor to employ labours with police verification. In case of any breach in security or loss of info the onus will entirely be on the vendor. Only Indian labours to be employed.

31. **Transportation.** The stores for shelter will be delivered at the consignee's end (FOR Loc) as per delivery schedule. The firm will make, its own arrangement to pay all taxes including transit insurance/octroi and other taxes as applicable, the cost thereof and will be responsible for defect free delivery of stores at destination. Labour charges for unloading the stores from your vehicles at consignee end and stocking in the stores yard of consignee will be borne by supplier.

32. **Notices.** Any notice required or permitted by the contract shall be written in the English language and may be delivered personally or may be sent by Email (**work-123@gov.in**) addressed to the last known address of the party to whom it is sent.

33. **Sample Approval.** Samples of the items to be used in the construction of the **Three (03) x Large Store Shelter** must be submitted to the accepting officer & Sample Approval must be taken within 15 days from the date of placement of supply order prior to commencement of Supply.